




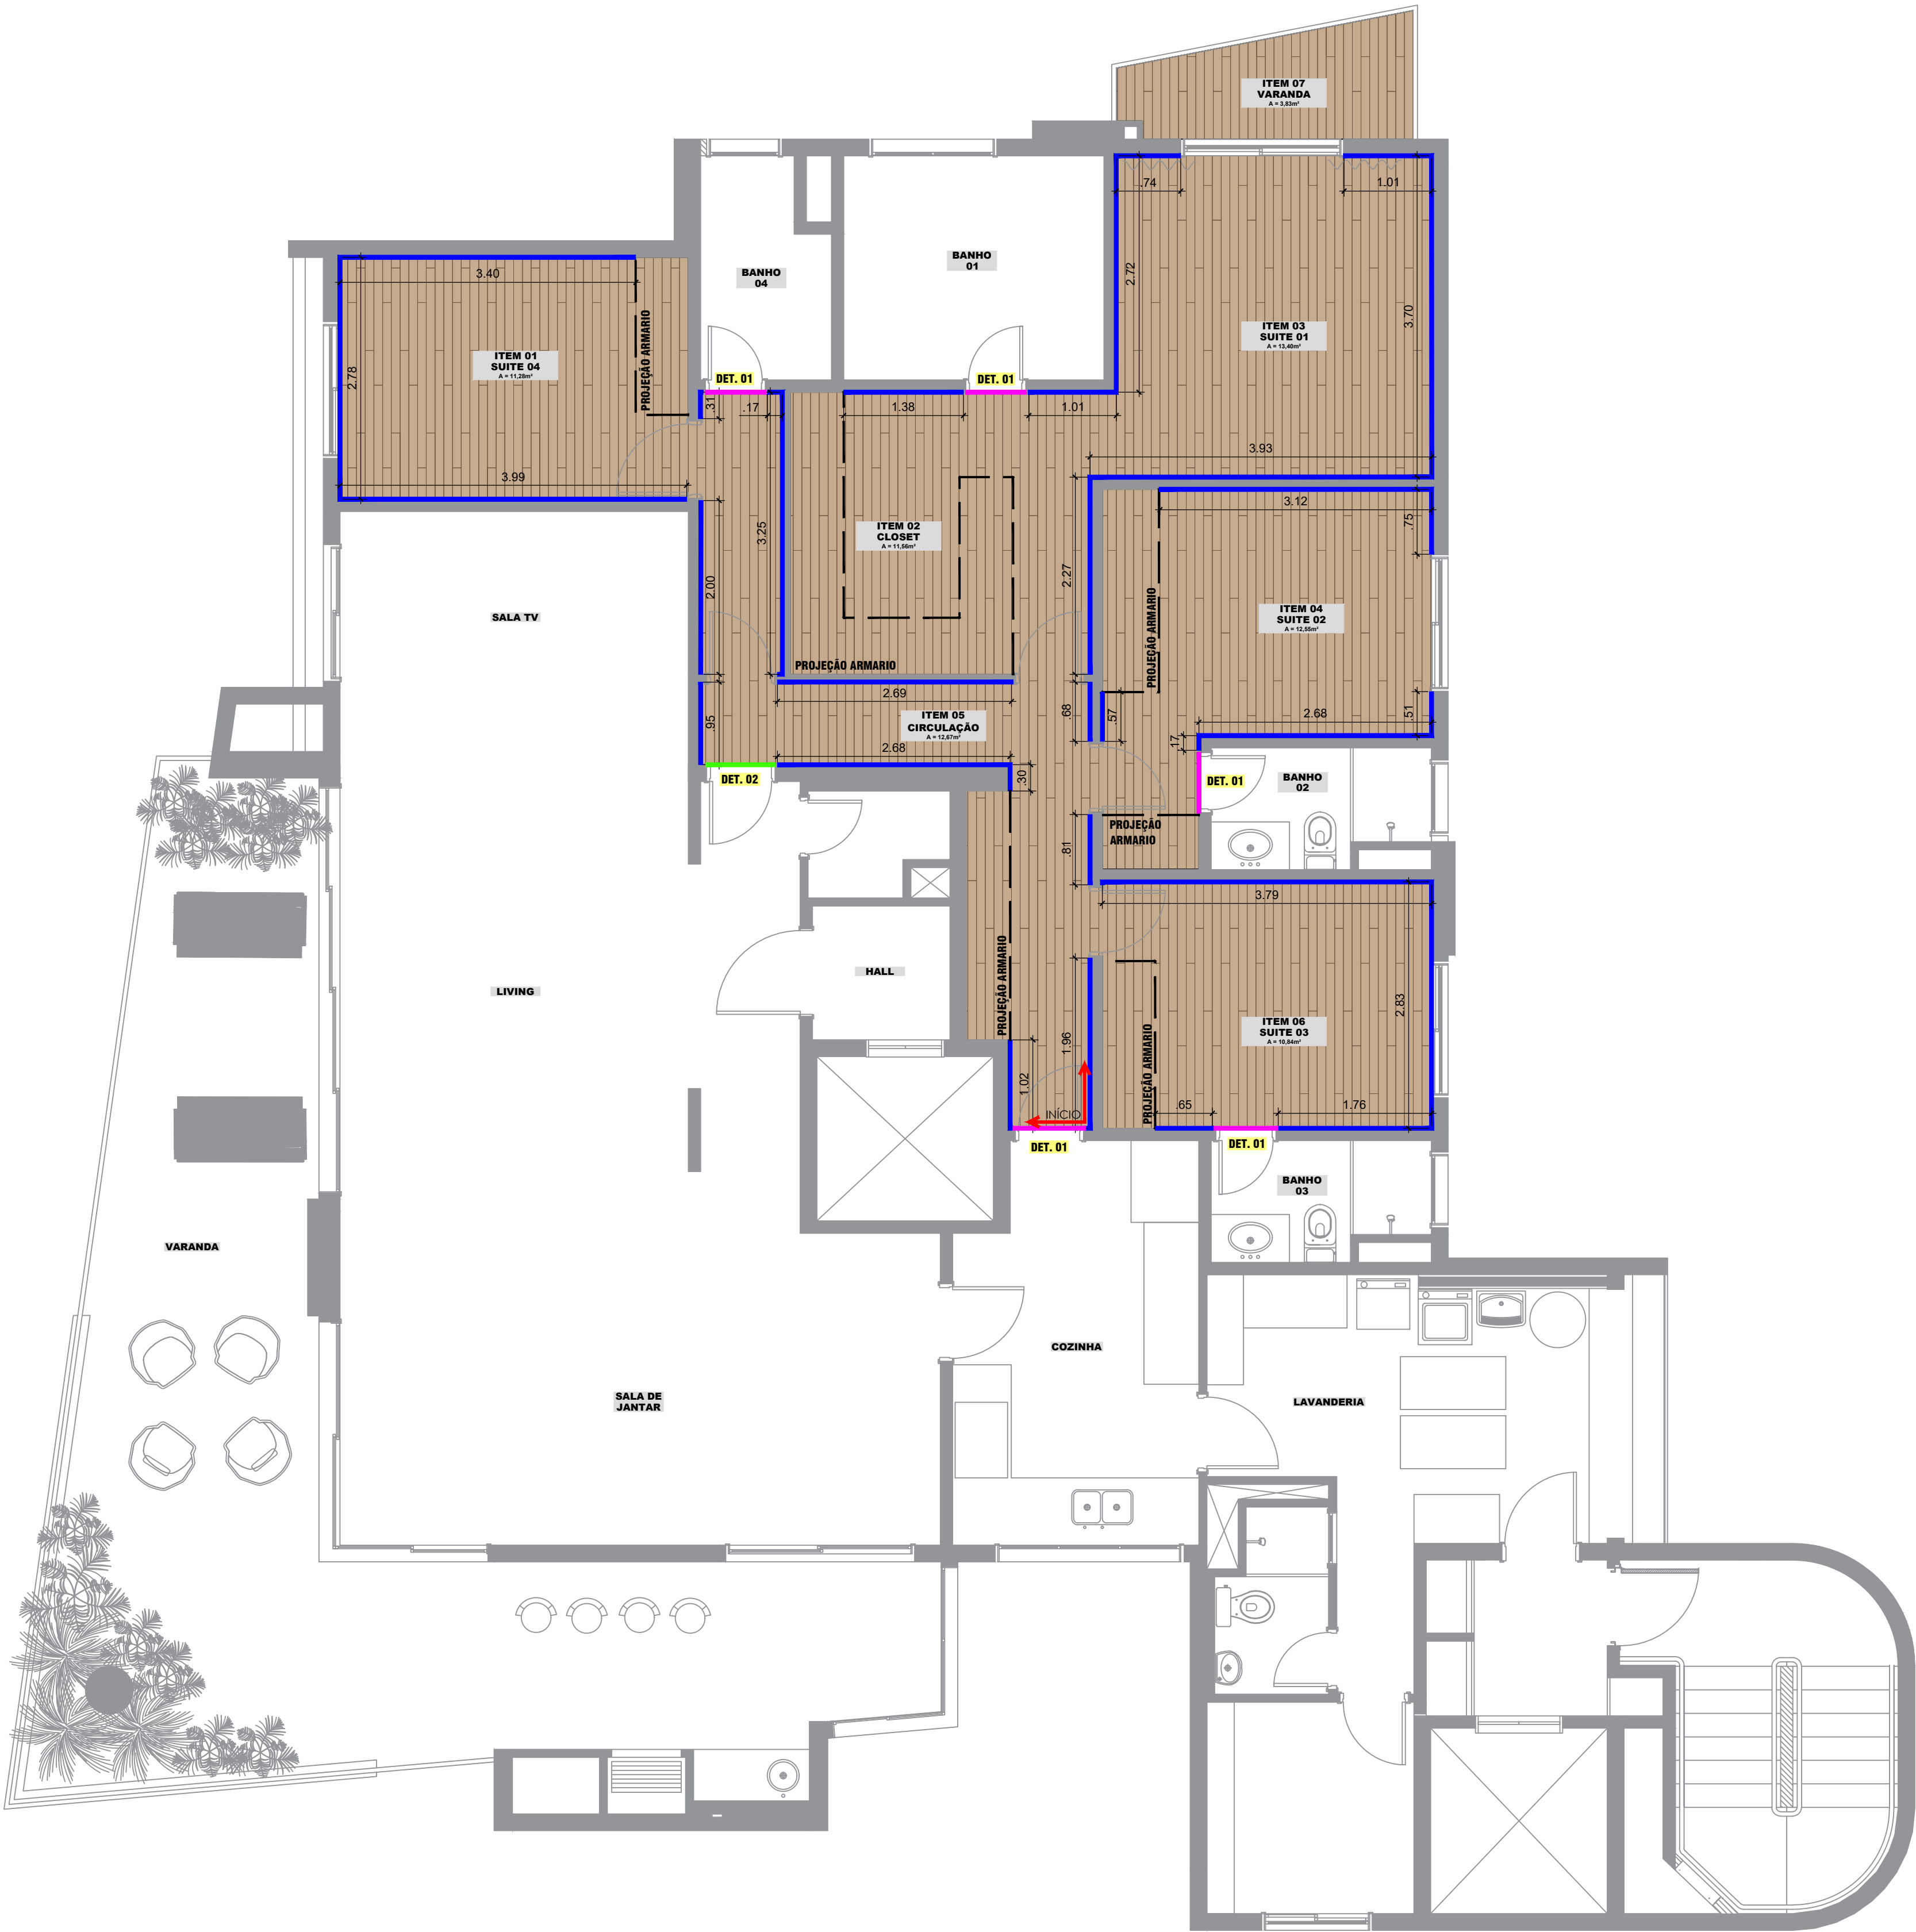


PLANTA DE PAGINAÇÃO DE PISO
1:50

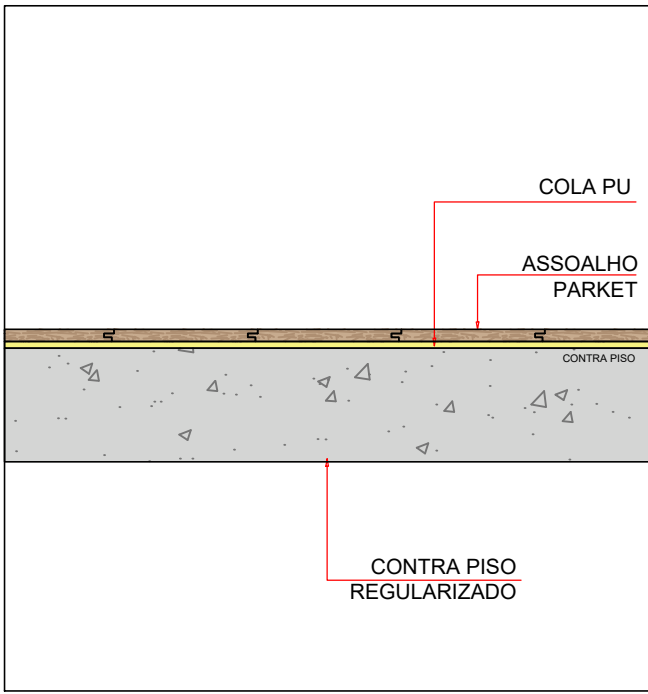


DET. FIXAÇÃO DE ASSOALHO
1:10

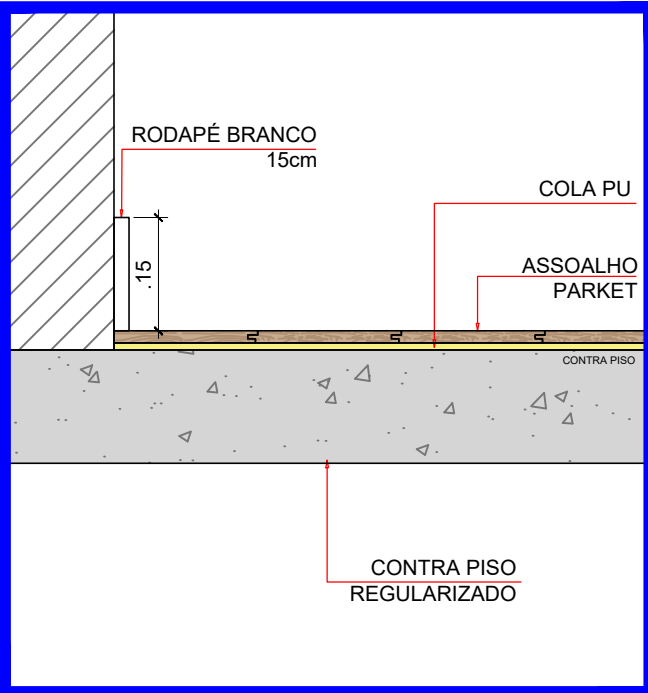

DET. RODAPÉ
1:10

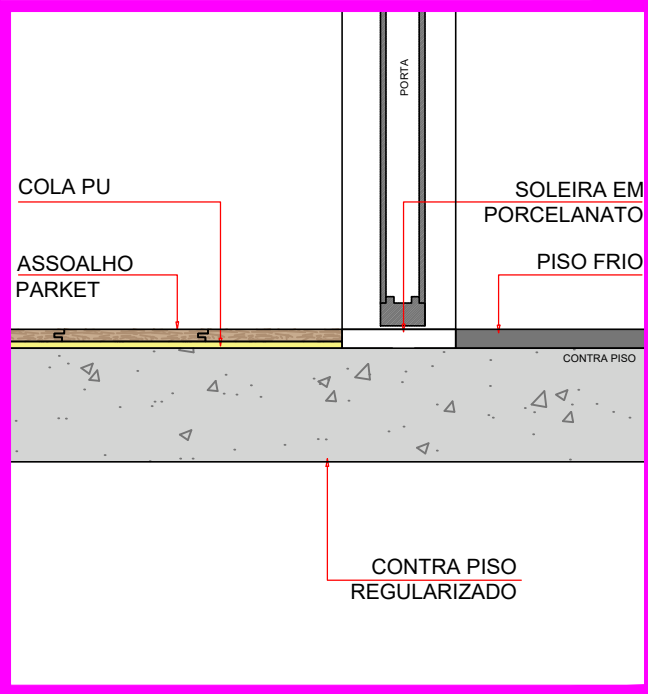

DET. 01 - TRANSIÇÃO DE PISO
1:10

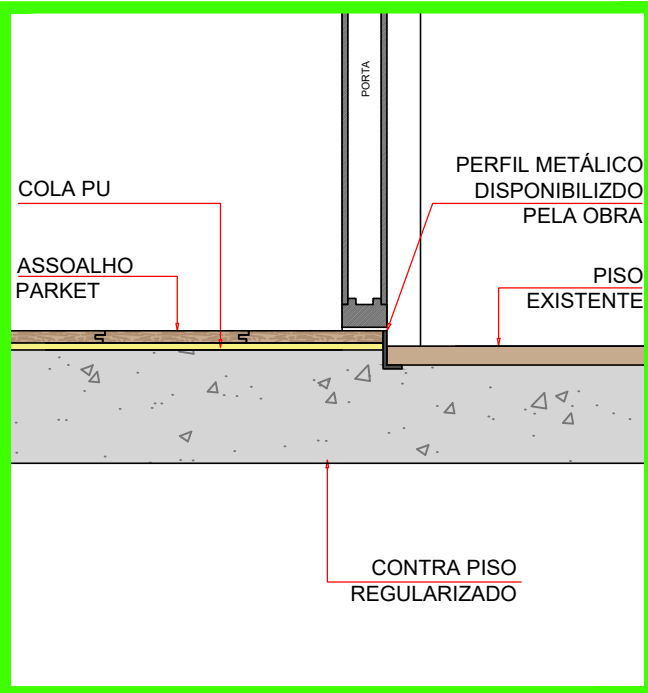

DET. 02 - TRANSIÇÃO DE PISO
1:10

ATENÇÃO!
PAGINAÇÃO A SER EXECUTADA COM REAPROVEITAMENTO DE 100% DO MATERIAL. PAGINAÇÃO EM PROJETO APENAS REPRESENTATIVA!!

RODAPÉ - AMBIENTES			
APARTAMENTO	ITEM 01A	SUITE 04	10,17ml
	ITEM 02A	CLOSET	4,66ml
	ITEM 03A	SUITE 01	12,10ml
	ITEM 04A	SUITE 02	7,80ml
	ITEM 05A	CIRCULAÇÃO	16,82ml
	ITEM 06A	SUITE 03	9,03ml
TOTAL PROJETO			65,52ml
TOTAL OBRA			65,52ml

PISO - AMBIENTES			
APARTAMENTO	ITEM 01	SUITE 04	11,28m²
	ITEM 02	CLOSET	11,56m²
	ITEM 03	SUITE 01	13,40m²
	ITEM 04	SUITE 02	12,55m²
	ITEM 05	CIRCULAÇÃO	12,67m²
	ITEM 06	SUITE 03	10,84m²
	ITEM 07	VARANDA	3,83m²
TOTAL PROJETO			76,13m²
TOTAL OBRA			76,13m²

LEGENDA DE ACABAMENTOS	
TIPO DE SERVIÇO:	
ASSOALHO COLADO COM COLA PU DIRETAMENTE NO CONTRAPISO	
DESCRIÇÃO DE MATERIAL:	
CUMARU 15/3 x 10 x 100-300CM	
RODAPÉ CURMURU - CORDÃO 2X2UMARU 15/3 x 10 x 100-300CM	

DATA	REV.	DESCRIÇÃO	PROJETISTA
25/08/2026	00	EXECUTIVO INICIAL	VINICIUS SANTOS
26/08/2026	01	INDICAÇÕES TRANSIÇÕES DE PISO	VINICIUS SANTOS
26/08/2026	02	REMOÇÃO PISO LAVABO E INCLUSÃO DO PISO VARANDA	VINICIUS SANTOS
05/10/2026	03	MUDANÇA TRANSIÇÃO DE PISO (DET. 02)	VINICIUS SANTOS
05/10/2026	04	RODAPÉ 15cm	VINICIUS SANTOS

11220

FELIPE CAMPOFIORITO

PROJETO DE INTERIORES

R. LISBOA, 144 - CERQUEIRA CESAR - SÃO PAULO - SP, 05413-000

ARQUITETURA

DATA PROJETO: AGOSTO / 2026

ESCALA

1/50

PARKET

PAGINAÇÃO DE PISO

FOLHA 01.01