

DET. 3.1.2 - RODAPÉ CORDÃO

ESC. 1:50

DET. 3.2 - RECORTE DE TOMADA

ESC. 1:50

DET. 3.2.2 - RECORTE PARA RALO

ESC. 1:50

DET. 3.4.2 - ENCONTRO DO PISO COM GUARDA-CORPO

ESC. 1:50

DET. 2.1.3 - ESPINHA DE PEIXE

ESC. 1:50

DET. 2.5 - PISO AQUECIDO

ESC. 1:50

DET. 3.4.1 - ENCONTRO DO PISO COM FORRO DE MADEIRA


ESC. 1:50

DET. 3.3 - ENTRETRILHO (TRILHO OCULTO)

ESC. 1:50

DET. 2.4.1 - PISO ELEVADO COM BARROTE

ESC. 1:50

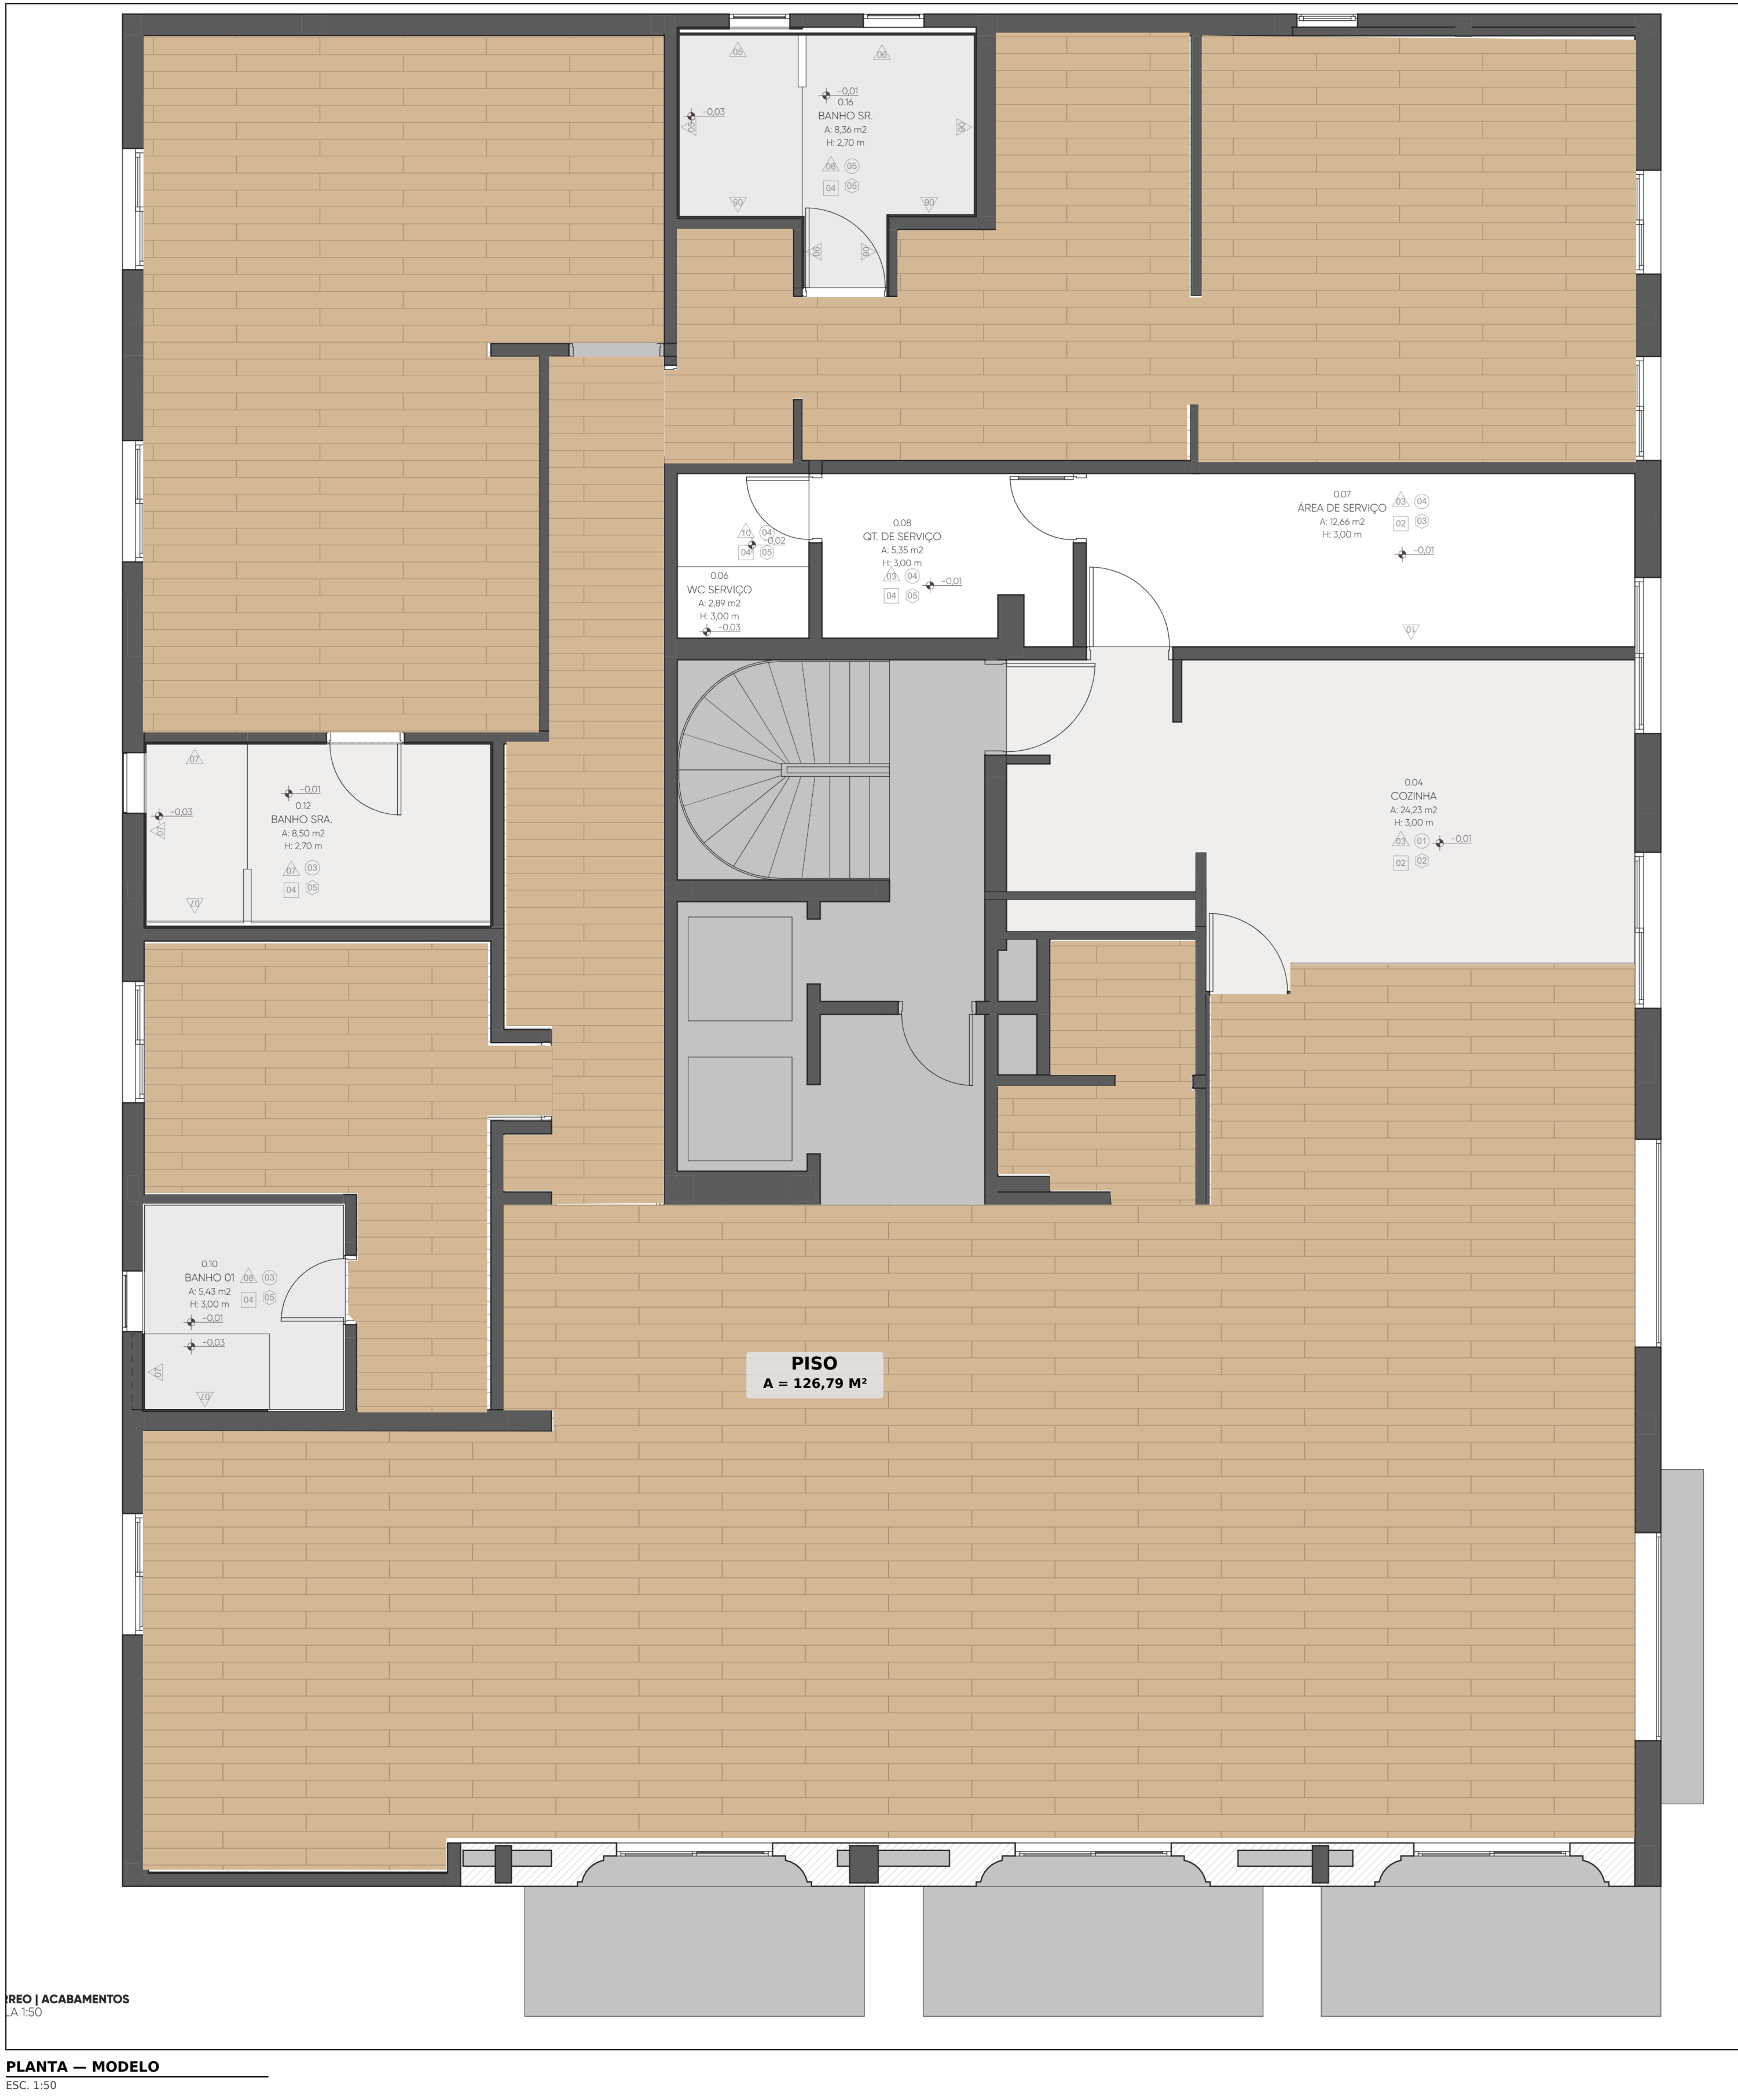

LEGENDA DE ACABAMENTOS			
TIPO DE SERVIÇO:			
ANTEPROJETO			
DESCRIÇÃO DE MATERIAL:			
DATA	REV.	DESCRIÇÃO	PROJETISTA
	00		

LIBERADO PARA PRODUÇÃO

PARKET