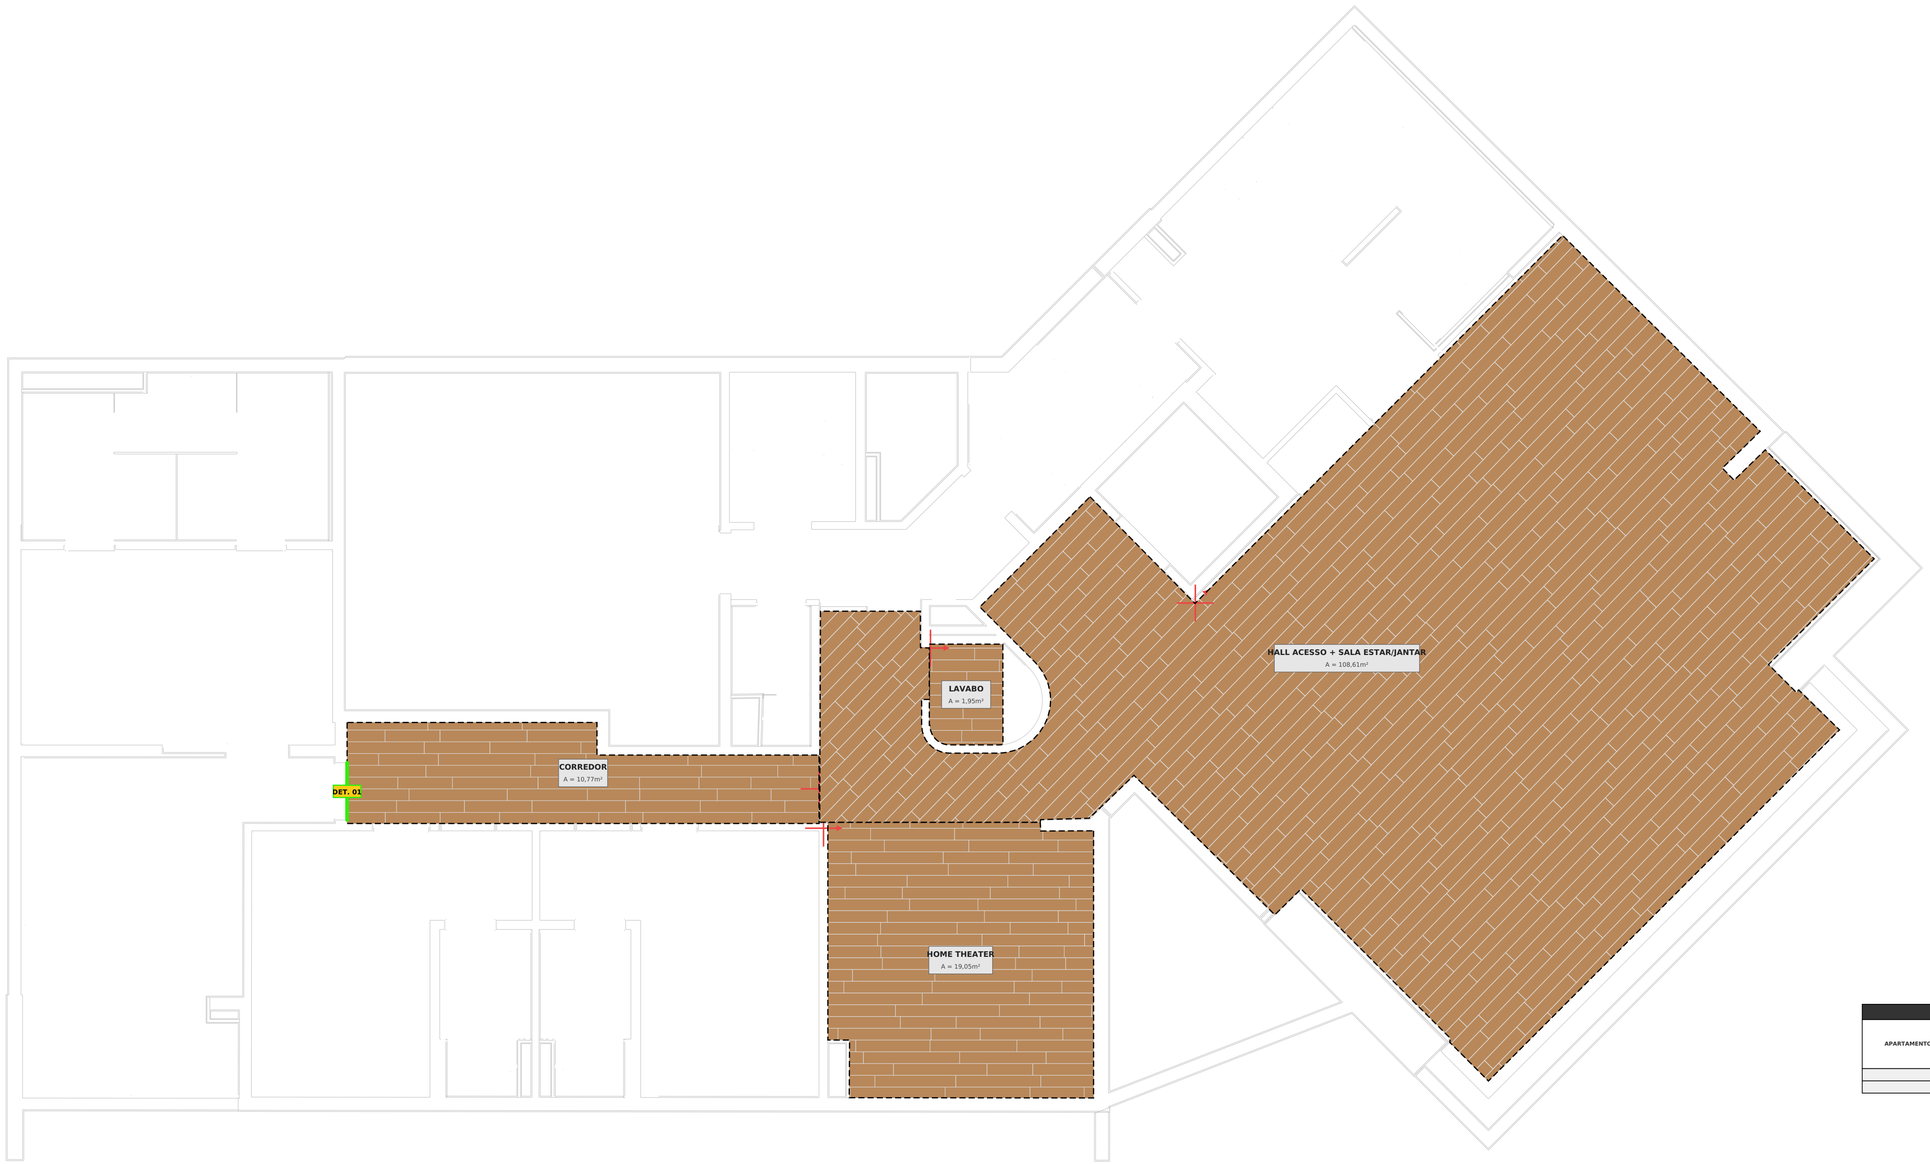

PLANTA BAIXA
1:50

FORRO - AMBIENTES			
APARTAMENTO	ITEM 01	CORREDOR	10,77 M²
	ITEM 02	HOME THEATER	19,05 M²
	ITEM 03	LAVABO	1,95 M²
	ITEM 04	HALL ACESSO + SALA ESTAR/JANTAR	108,61 M²
		TOTAL PAVIMENTO	140,39 M²
		TOTAL OBRA	140,39 M²

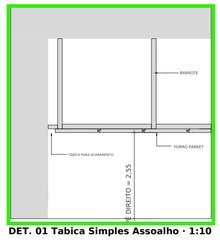

DET. 01 Tabica Simples Assoalho · 1:10

LEGENDA DE ACABAMENTOS

TIPO DE SERVIÇO:
PRANCHA DE FORRO
DESCRIÇÃO DE MATERIAL:
LOURO PARDO

DATA	REV.	DESCRIÇÃO	PROJETISTA

LIBERADO PARA PRODUÇÃO

PARKET

PAGINAÇÃO DE FORRO FOLHA 01.01

CLIENTE:
ANDRÉ CAMPEDELI

NÚMERO DE OS: 1565
ENDEREÇO: RUA TAL
ARQUITETURA: BLABLABLA
DATA PARKET: ABRIL/2026
ESCALA: 1:50

A1 (841 mm x 594 mm)