




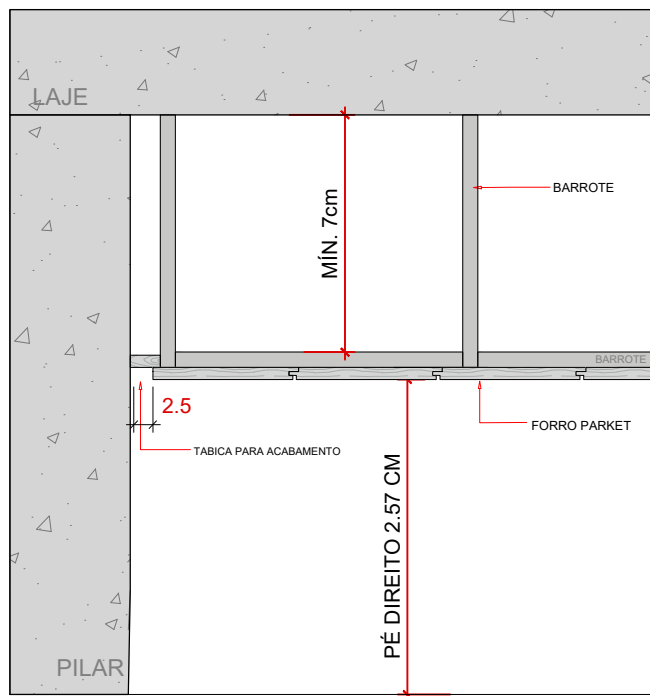


DET. 01 - TABICA SIMPLES
1:10

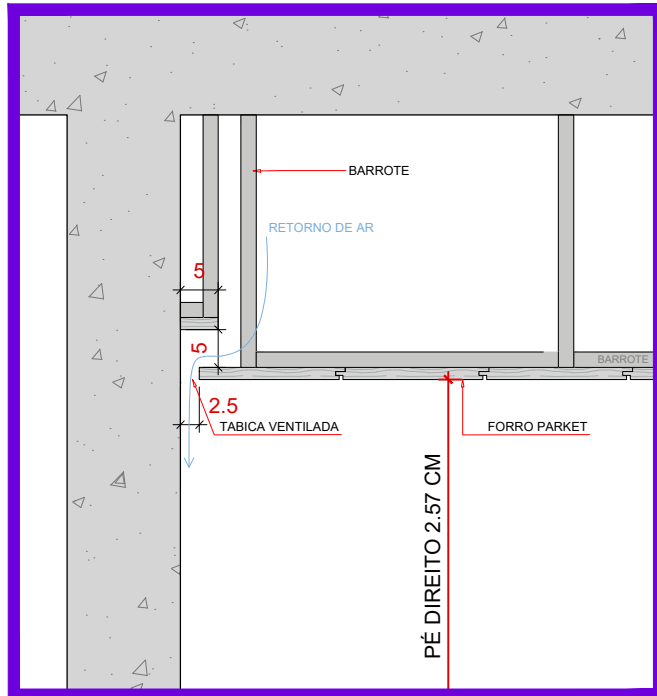


DET. 02 - TABICA SIMPLES COM RETORNO
1:10

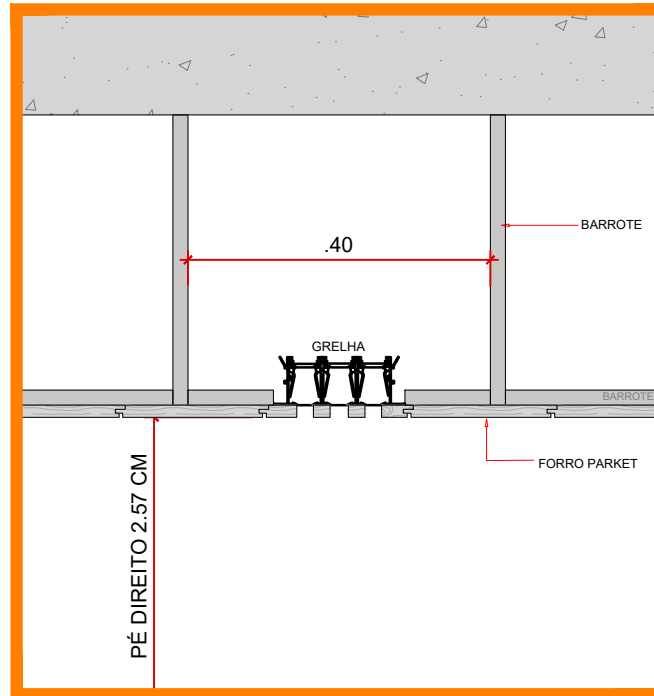


DET. 03 - GRELHA
1:10

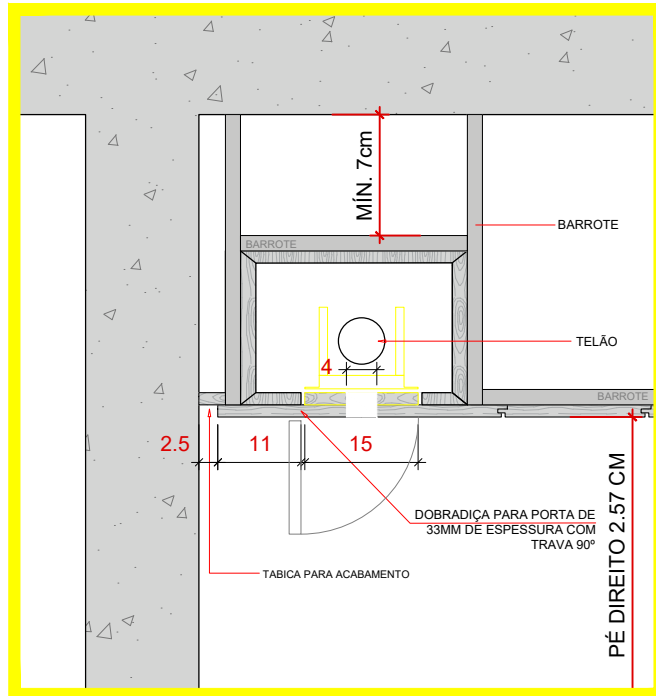


DET. 04 - TELÃO EMBUTIDO
1:10

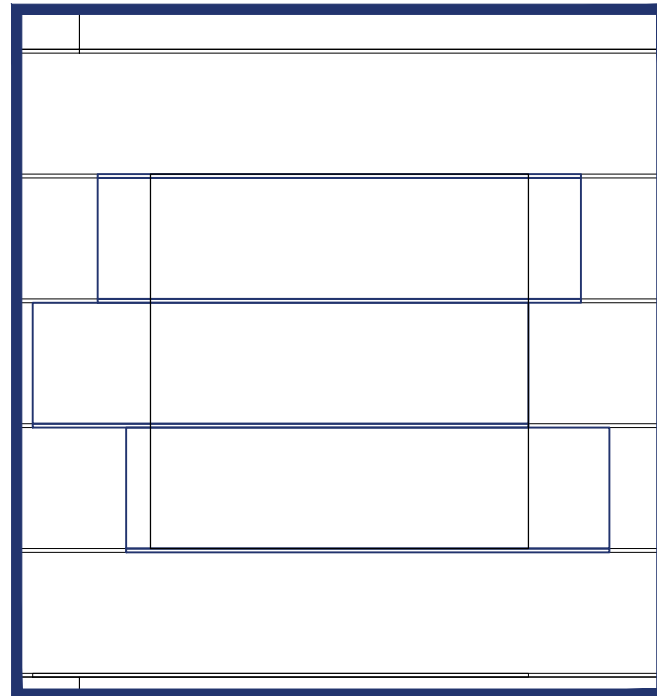


DET. 05 - ALÇAPÃO
1:10

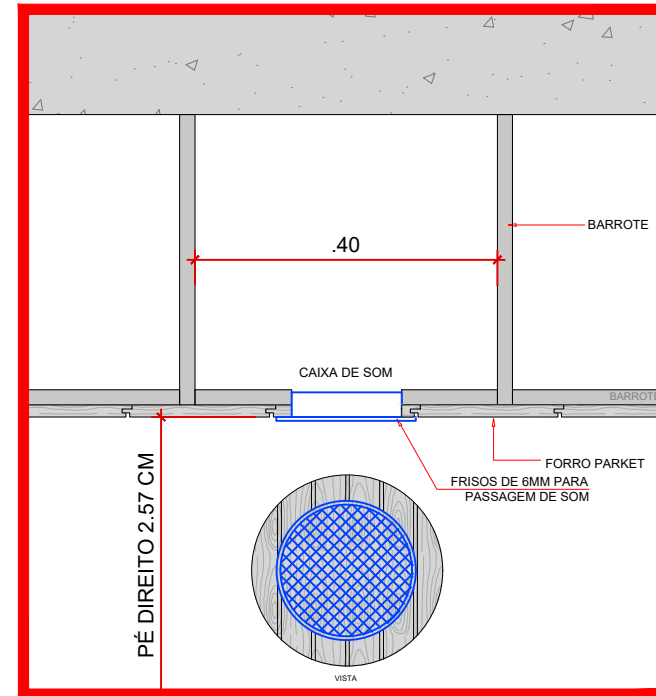


DET. 06 - CAIXA DE SOM
1:10

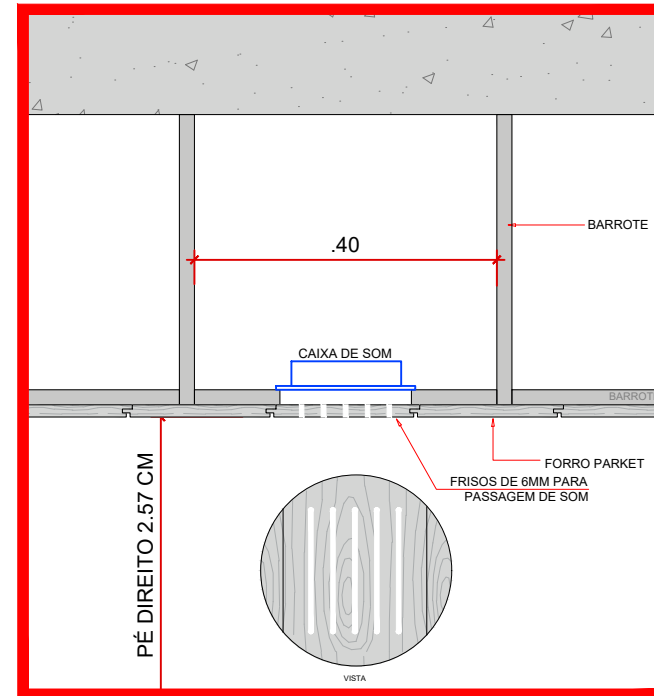


DET. 07 - CAIXA DE SOM
1:10

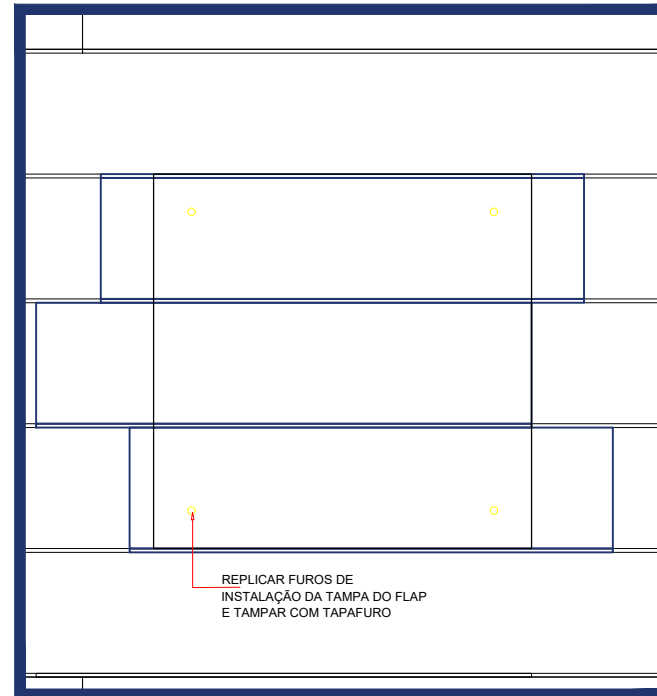


DET. 08 - FLAP PROJETOR
1:10

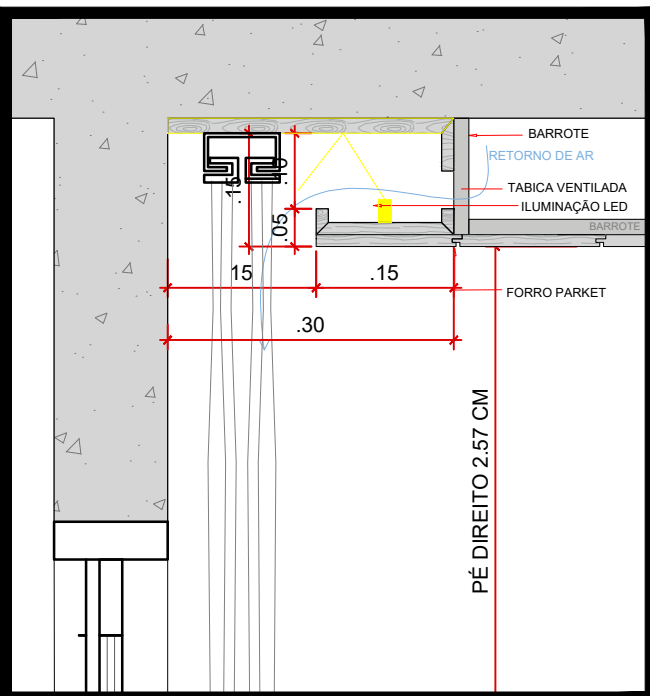


DET. 09 - CORTINEIRO ILUMINADO COM RETORNO DE AR
1:10

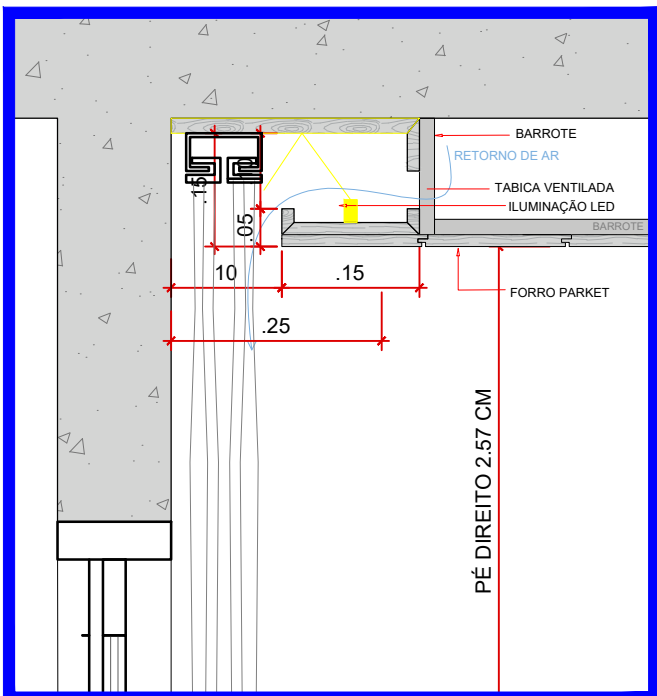

DET. 10 - CORTINEIRO ILUMINADO COM RETORNO DE AR
1:10

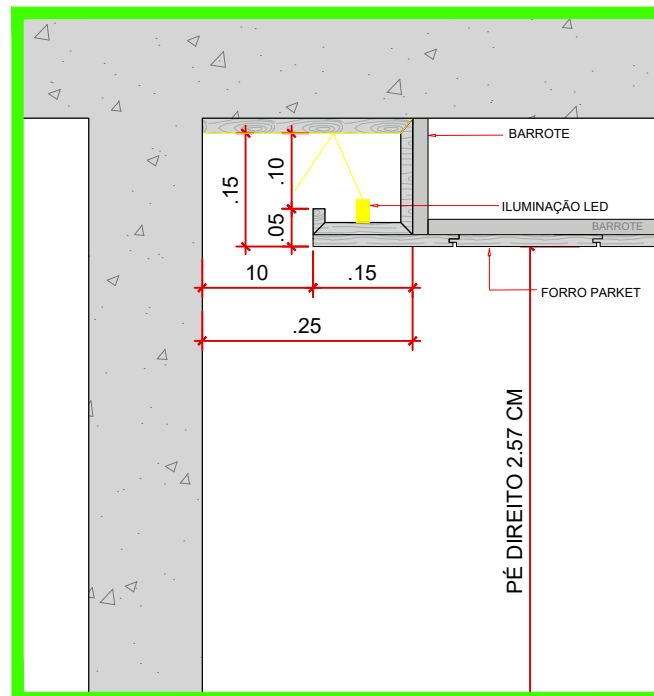

DET. 11 - SANCA ILUMINADA
1:10

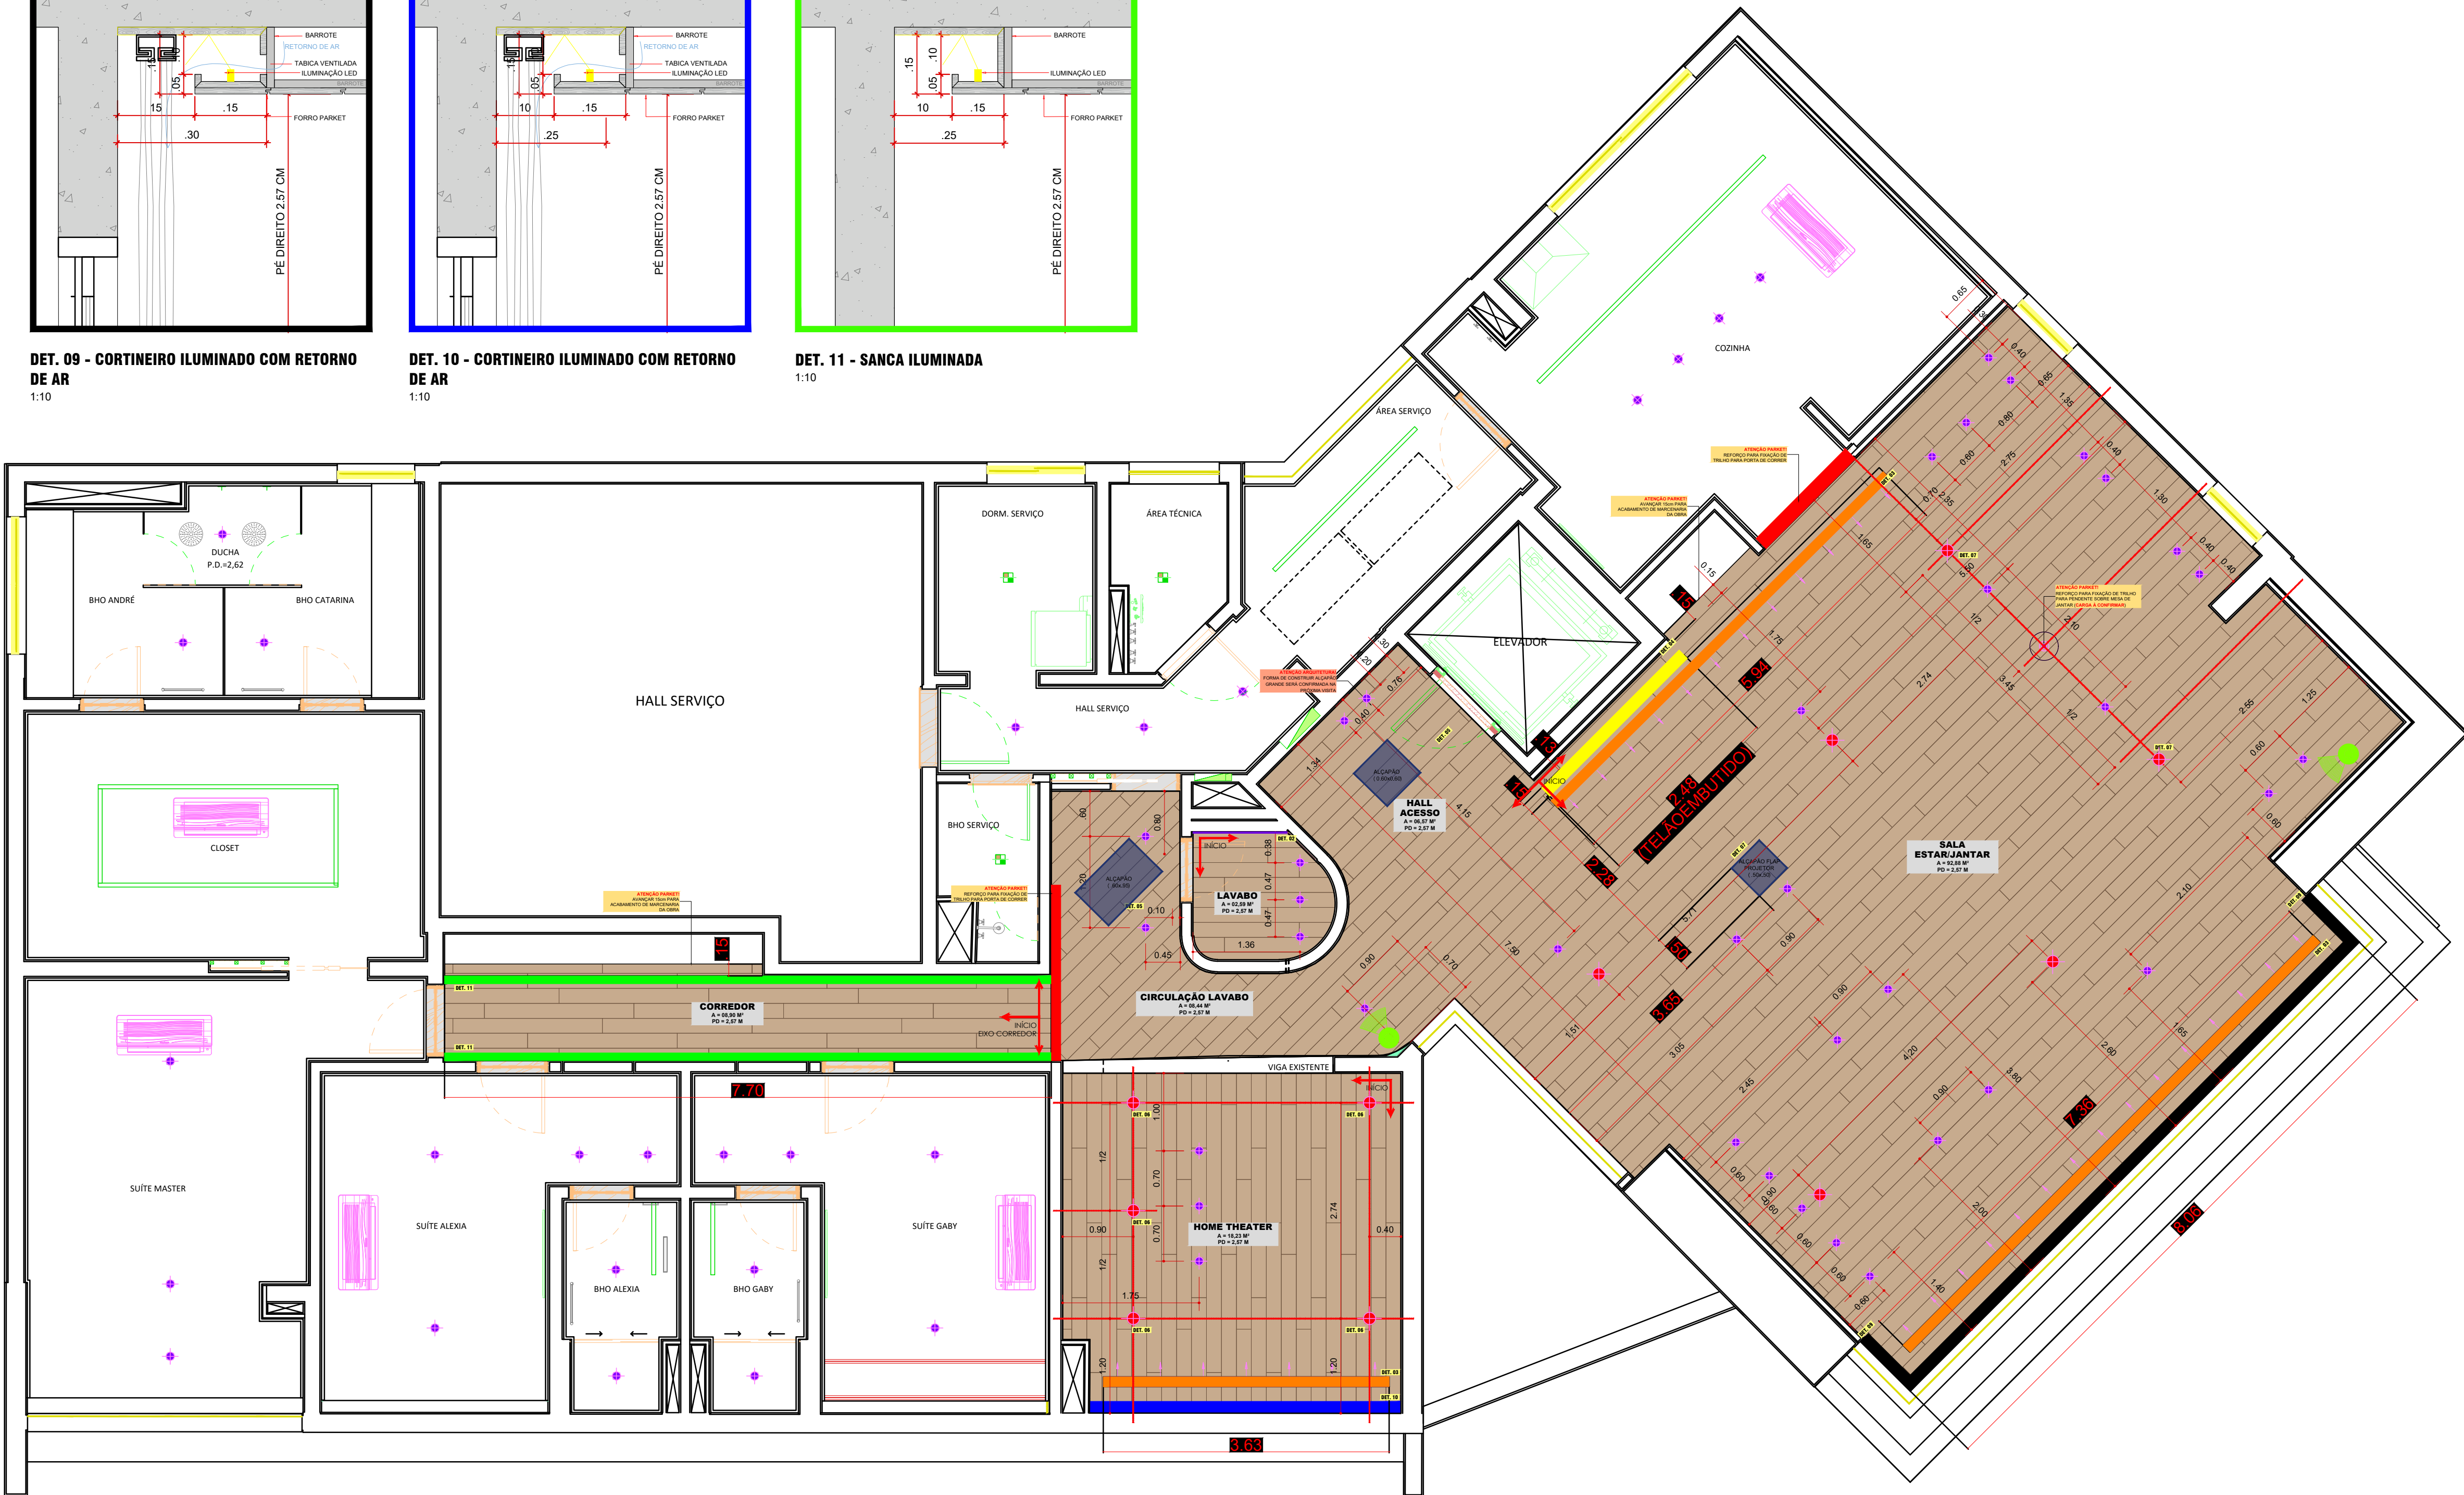

CAIXA DE SOM - AMBIENTES			
APARTAMENTO	ITEM 02E	SALA ESTAR / JANTAR	06 UNID.
	ITEM 05E	HOME THEATER	05 UNID.
TOTAL PAVIMENTO			11 UNID.
TOTAL OBRA			11 UNID.

ALÇAPÃO - AMBIENTES			
APARTAMENTO	ITEM 01D	HALL ACESSO	01 UNID.
	ITEM 02D	SALA ESTAR / JANTAR	01 UNID.
	ITEM 03D	CIRCULAÇÃO LAVABO	01 UNID.
TOTAL PAVIMENTO			03 UNID.
TOTAL OBRA			03 UNID.

GRELHAS - AMBIENTES			
APARTAMENTO	ITEM 02C	SALA ESTAR / JANTAR (GRELHAS)	13,30ML
	ITEM 05C	HOME THEATER	03,63ML
TOTAL OBRA			19,41ML

RECORTES DIVERSOS - AMBIENTES			
APARTAMENTO	ITEM 01B	HALL ACESSO	02 UNID.
	ITEM 02B	SALA ESTAR / JANTAR	28 UNID.
	ITEM 03B	CIRCULAÇÃO LAVABO	04 UNID.
	ITEM 04B	LAVABO	03 UNID.
	ITEM 05B	HOME THEATER	03 UNID.
TOTAL PAVIMENTO			40 UNID.
TOTAL OBRA			40 UNID.

CORTINEIRO / SANCA			
APARTAMENTO	DET. 06 (AZUL CLARO)		08,06ML
	ITEM 02A	SALA ESTAR / JANTAR	
	DET. 07 (AZUL ESCURO)		03,63ML
	ITEM 05A	HOME THEATER	
	ITEM 06A	CORREDOR	15,40ML
TOTAL PAVIMENTO			27,09ML
TOTAL OBRA			27,09ML

FORRO - AMBIENTES			
APARTAMENTO	ITEM 01	HALL ACESSO	06,57 M²
	ITEM 02	SALA ESTAR / JANTAR	92,88 M²
	ITEM 03	CIRCULAÇÃO LAVABO	08,44 M²
	ITEM 04	LAVABO	02,59 M²
	ITEM 05	HOME THEATER	18,28 M²
	ITEM 06	CORREDOR	08,90 M²
TOTAL PAVIMENTO			137,66 M²
TOTAL OBRA			137,66 M²

LEGENDA DE ACABAMENTOS			
TIPO DE SERVIÇO:			
ASSOALHO COLADO COM COLA PU DIRETAMENTE NO CONTRAPISO			
DESCRIÇÃO DE MATERIAL:			
LOURO PARDO MULTI PREMIUM PERSONALIZADO 1,5 x 18,5" BRUNHA x 80 À 300 CM (CONFORME PROTÓTIPO DE OBRA)			
DATA	REV.	DESCRIÇÃO	PROJETISTA
22.10.2025	00	EXECUTIVO INICIAL	ALEXSANDRO F
23.10.2025	01	ADITIVO DE CAIXAS DE SOM E REVISÃO DET. FLAP TELÃO	ALEXSANDRO F
10.11.2025	02	REVISÕES CONFORME ARQUIVO COMENTADO POR EMAIL	ALEXSANDRO F
27.11.2025	03	CONFORME REVISÕES APÓS VISITA	ALEXSANDRO F

PARKET

PAGINAÇÃO DE FORRO FOLHA 01.01