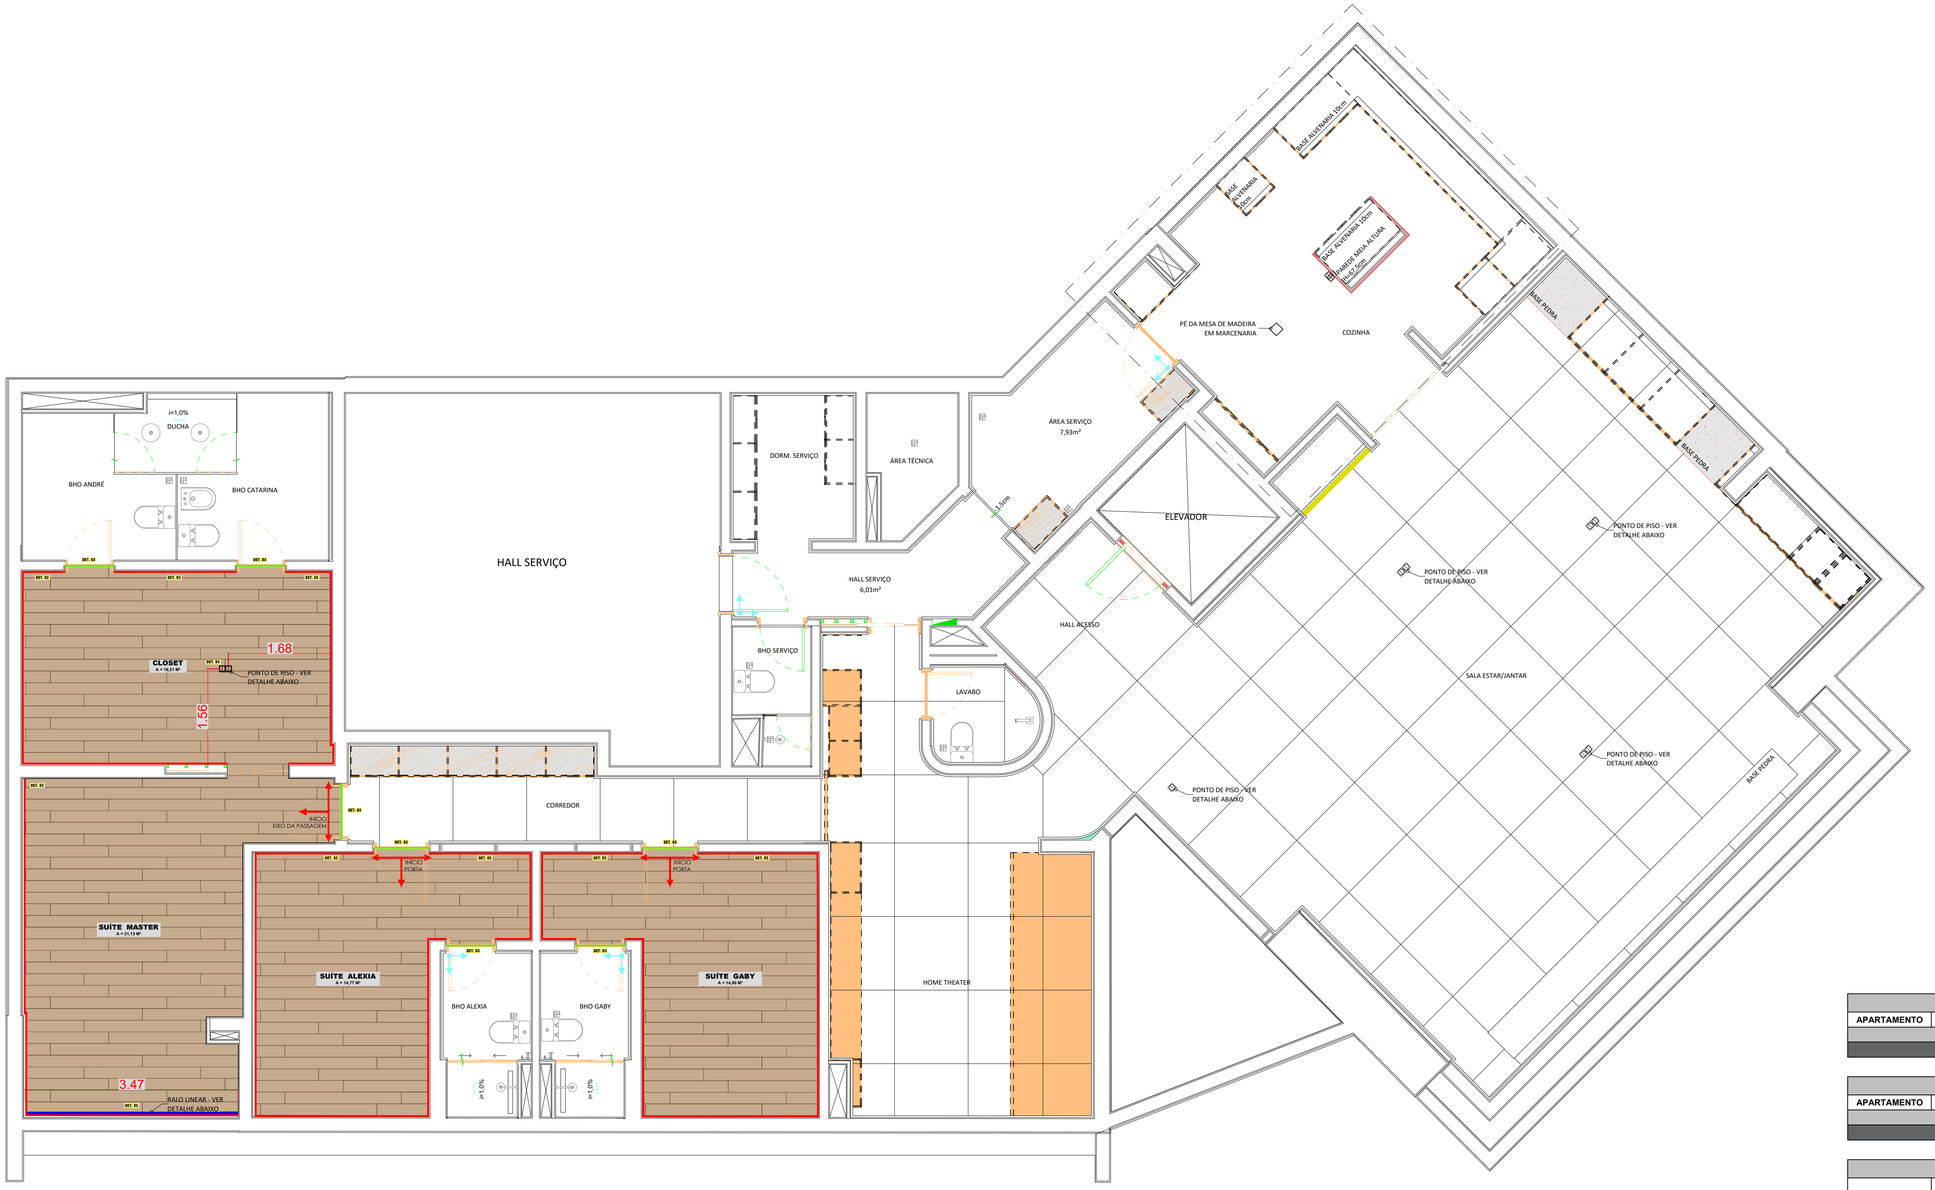

PLANTA BAIXA
1:50

RECORTES DIVERSOS - AMBIENTES			
APARTAMENTO	ITEM 01C	SUÍTE MASTER	03,47 ML
TOTAL PAVIMENTO			03,47 ML
TOTAL OBRA			03,47 ML

RECORTES DIVERSOS - AMBIENTES			
APARTAMENTO	ITEM 02C	CLOSET	01 UNID.
TOTAL PAVIMENTO			01 UNID.
TOTAL OBRA			01 UNID.

PISO - AMBIENTES			
APARTAMENTO	ITEM 01	SUÍTE MASTER	21,13 M²
	ITEM 02	CLOSET	16,31 M²
	ITEM 03	SUÍTE ALEXIA	14,77 M²
	ITEM 04	SUÍTE GABY	14,90 M²
TOTAL PAVIMENTO			67,11 M²
TOTAL OBRA			67,11 M²

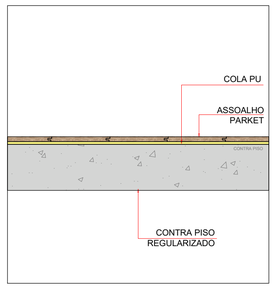

DET. 01 - FIXAÇÃO DE ASSOALHO
1:10

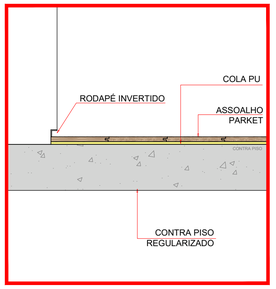

DET. 02 - RODAPÉ INVERTIDO
1:10

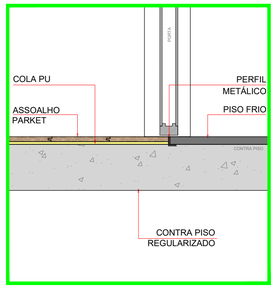

DET. 03 - TRANSIÇÃO DE PISO
1:10

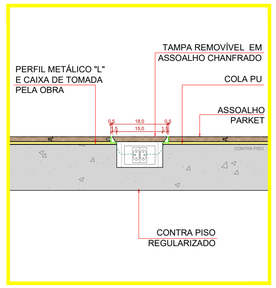

DET. 04 - TOMADA COM TAMPA REMOVÍVEL
1:10

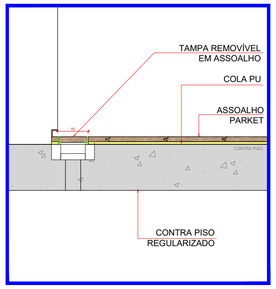

DET. 05 - RALO LINEAR COM TAMPA REMOVÍVEL
1:10

LEGENDA DE ACABAMENTOS

TIPO DE SERVIÇO:
ASSOALHO COLADO COM COLA PU DIRETAMENTE NO CONTRAPISO

DESCRIÇÃO DE MATERIAL:
LOURO PARDO MULTI PREMIUM 1,5 x 19 x 80 À 300 CM

DATA	REV.	DESCRIÇÃO	PROJETISTA
22.10.2025	00	EXECUTIVO INICIAL	ALEXSANDRO F
10.11.2025	01	RETIRADA DE BASE DE PEDRA SUÍTE ALEXIA	ALEXSANDRO F

PARKET

PAGINAÇÃO DE PISO

FOLHA 01.01

ANDRÉ MARCOS CAMPEDELLI

2270 RUA PADRE JOÃO MANUEL, 574, 4º ANDAR - CERQUEIRA CESAR, SÃO PAULO - SP

soek.ARQUITETURA
OUTUBRO / 2025
1:50

A1 (841 mm x 594 mm)