




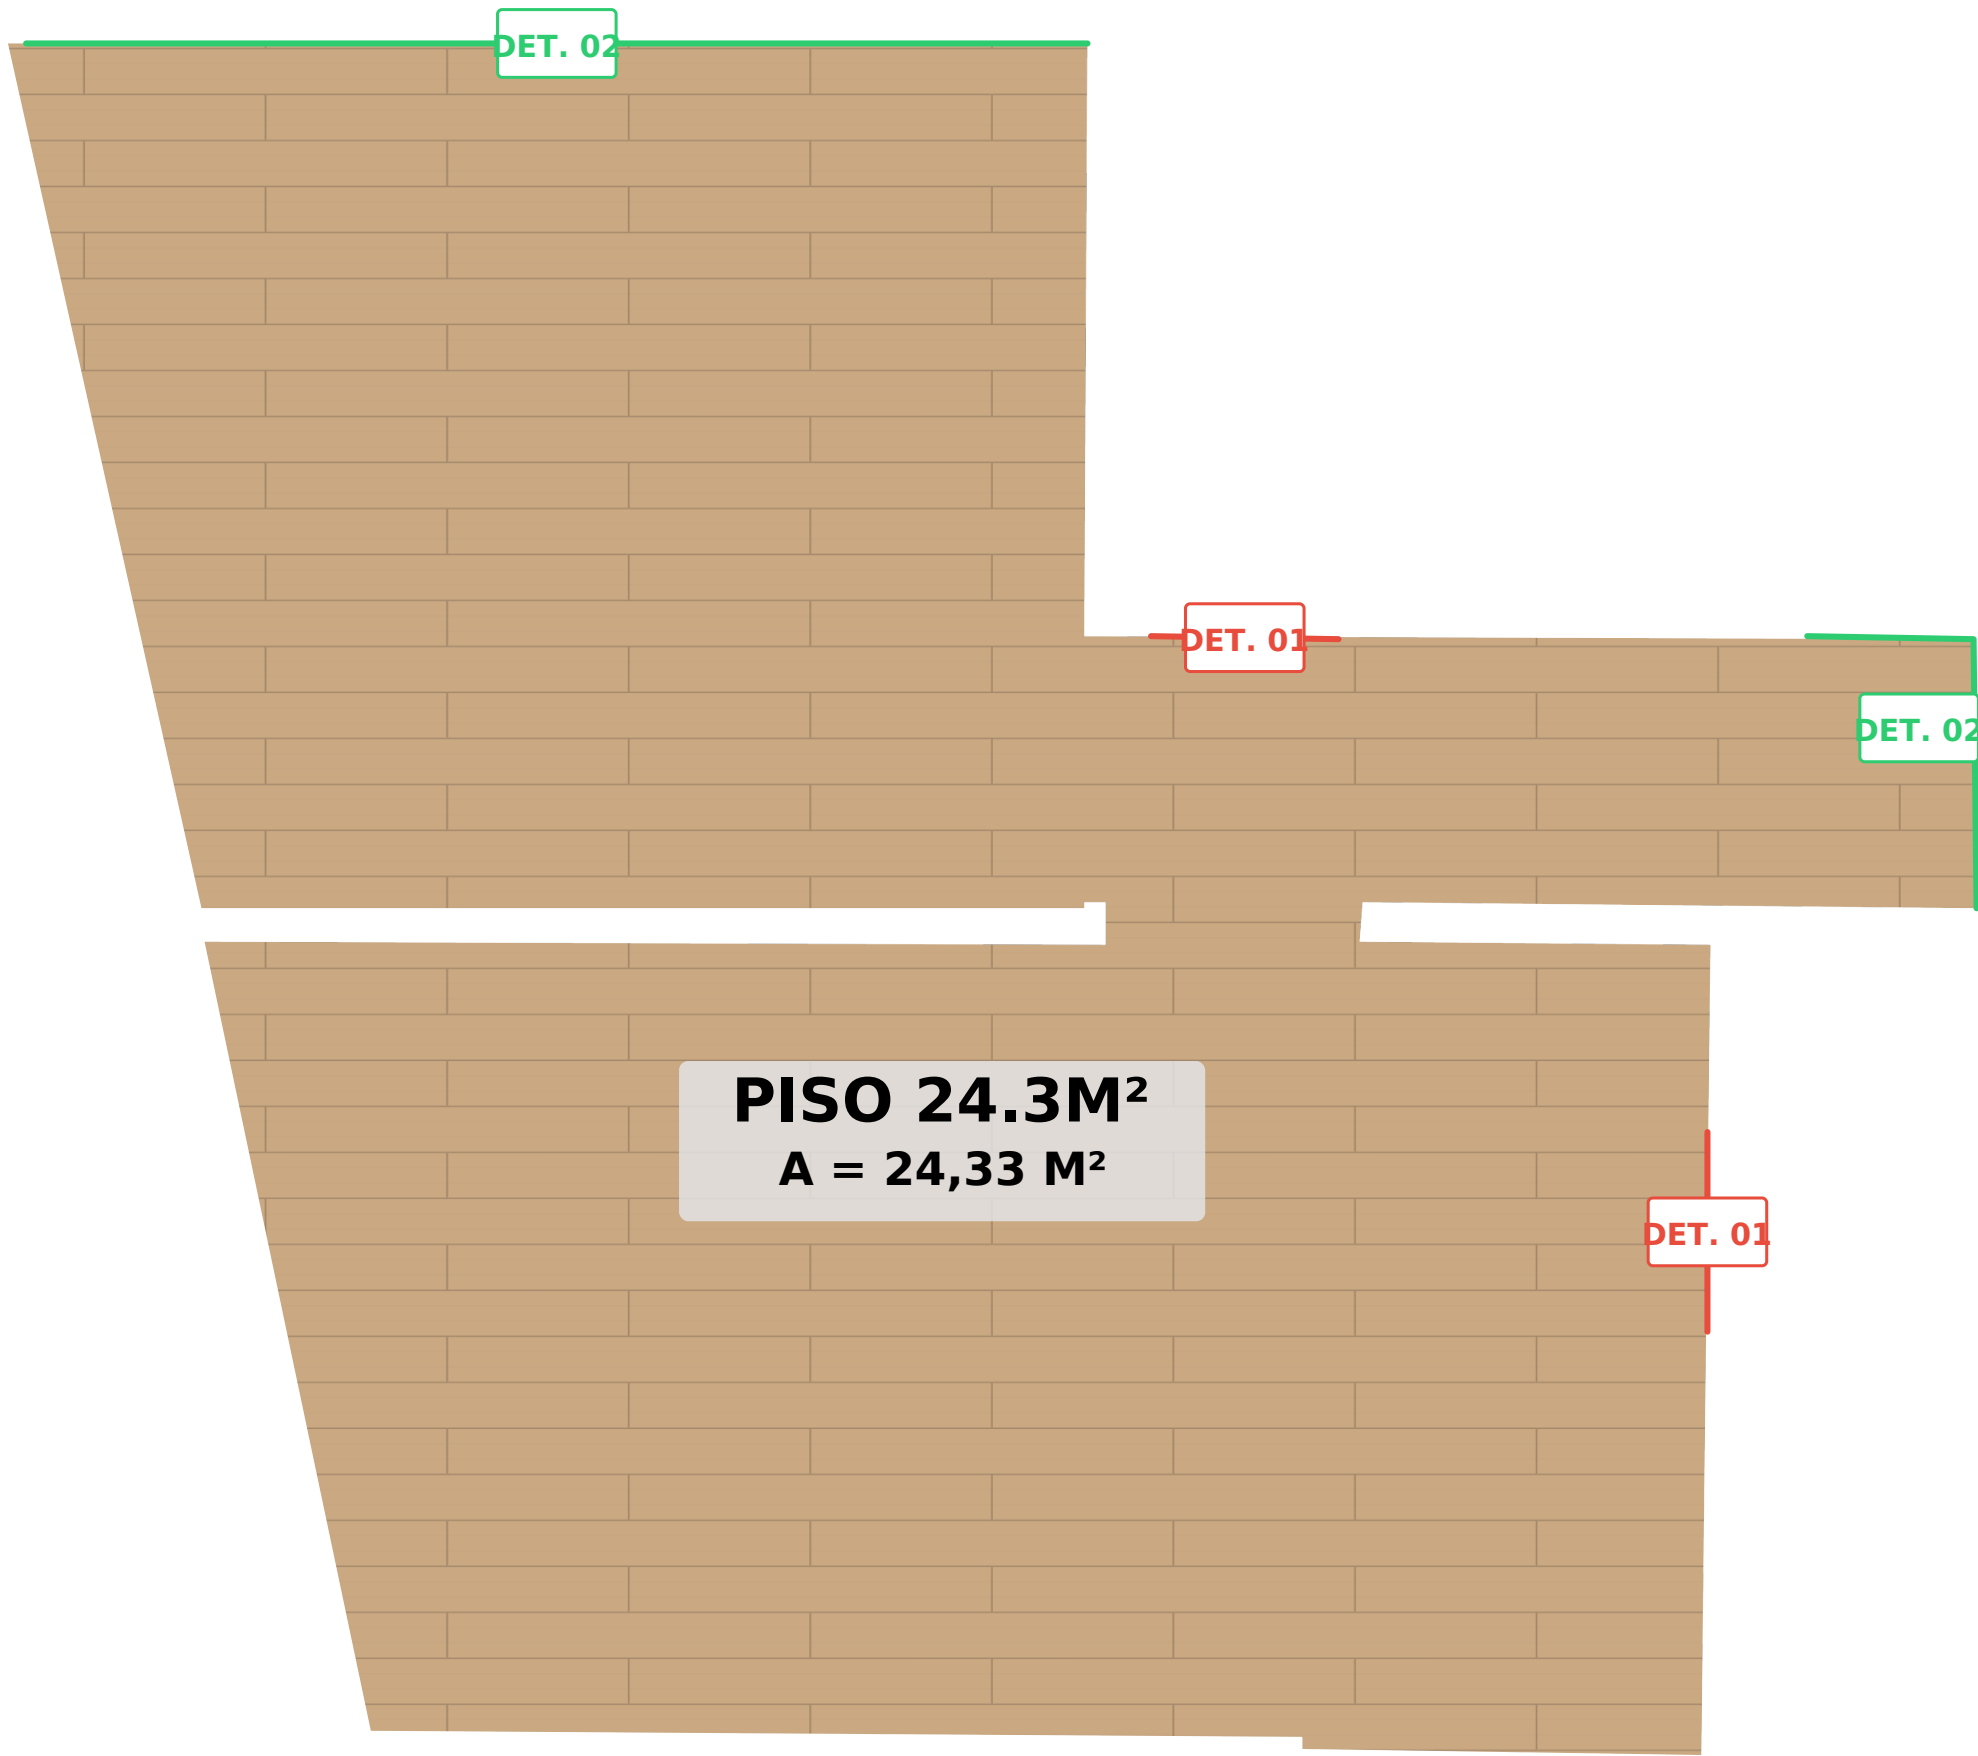

PLANTA — PISO
ESC. 1:25

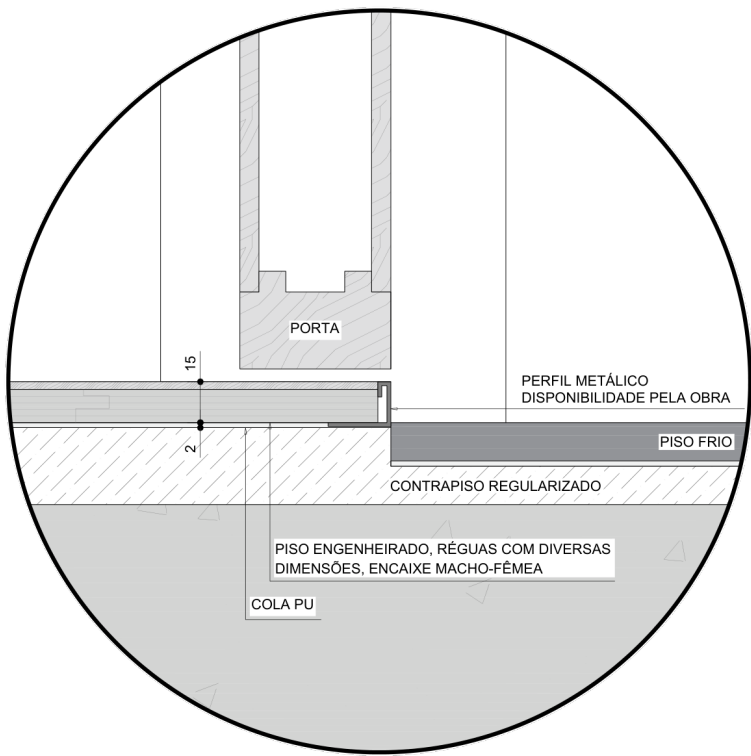

DET. 01 - TRANSIÇÃO DE PISO EM PERFIL METÁLICO COM DÉSNIVEL
ESC. 1:10

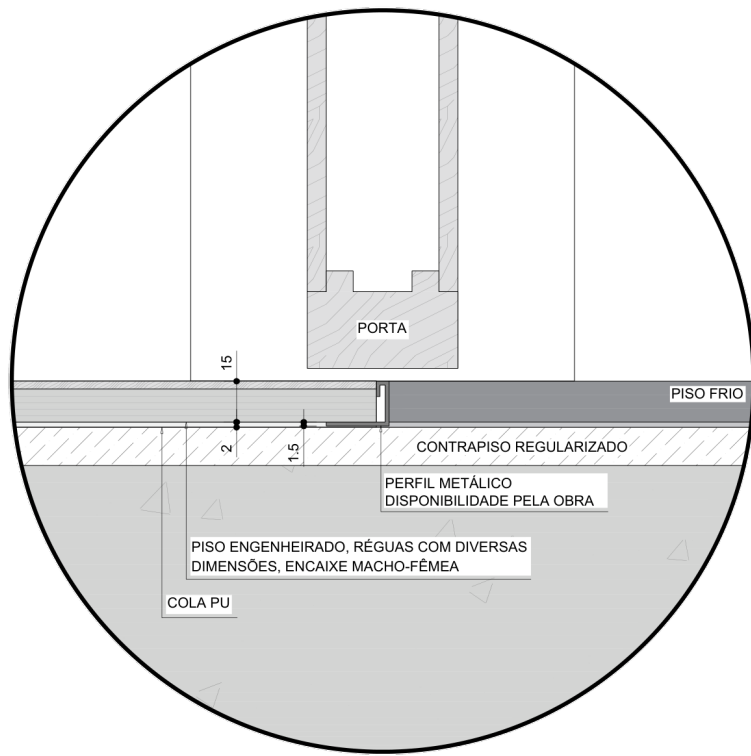

DET. 02 - TRANSIÇÃO DE PISO EM PERFIL METÁLICO
ESC. 1:10

LEGENDA DE ACABAMENTOS			
TIPO DE SERVIÇO:			
PISO			
DESCRIÇÃO DE MATERIAL:			
CUMARU PREMIUM MULTI 1, 5*15*40A220CM			
DATA	REV.	DESCRIÇÃO	PROJETISTA
	00		

LIBERADO PARA PRODUÇÃO

PARKET